Furnished floor plan / R09

Scale 1:65 at A3. Shared layout for CAD and website.



ALL DIMENSIONS mm / WALLS >= 140 / STRUCTURAL COLUMNS RETAINED

140 mm WALLS

All wall and partition bands are at least 140 mm thick. The eight structural columns retain their original positions and sizes.

BEDROOMS MATCH

Main and children bedrooms are drawn from the same furniture records as the website, including both beds, wardrobe runs, dressing table and retained study desk.

CHILD DOOR

D07 retains its 850 mm nominal width. It opens inward to the left of a person entering from the hall.

RESTORED ENTRANCES

The master and children openings return to their earlier wall positions. D05 stays 800 mm wide; the short master entry return is removed.

CORRECTED WARDROBE

M04 is one complete 2220 wide x 650 deep x 2150 high unit, as corrected by the owner. C02 extends to 2850 mm; C12 reduces to 800 mm to clear D07.


CHECKED

Native AutoCAD audit reports zero errors. Floor furniture and door swing sectors clear walls and columns. This is the R09 review set.

Print A3 at 100%. Dimensions in millimetres.

Main bedroom / corrected wardrobe and entrance

Scale 1:25 at A3. Owner-confirmed width and height.

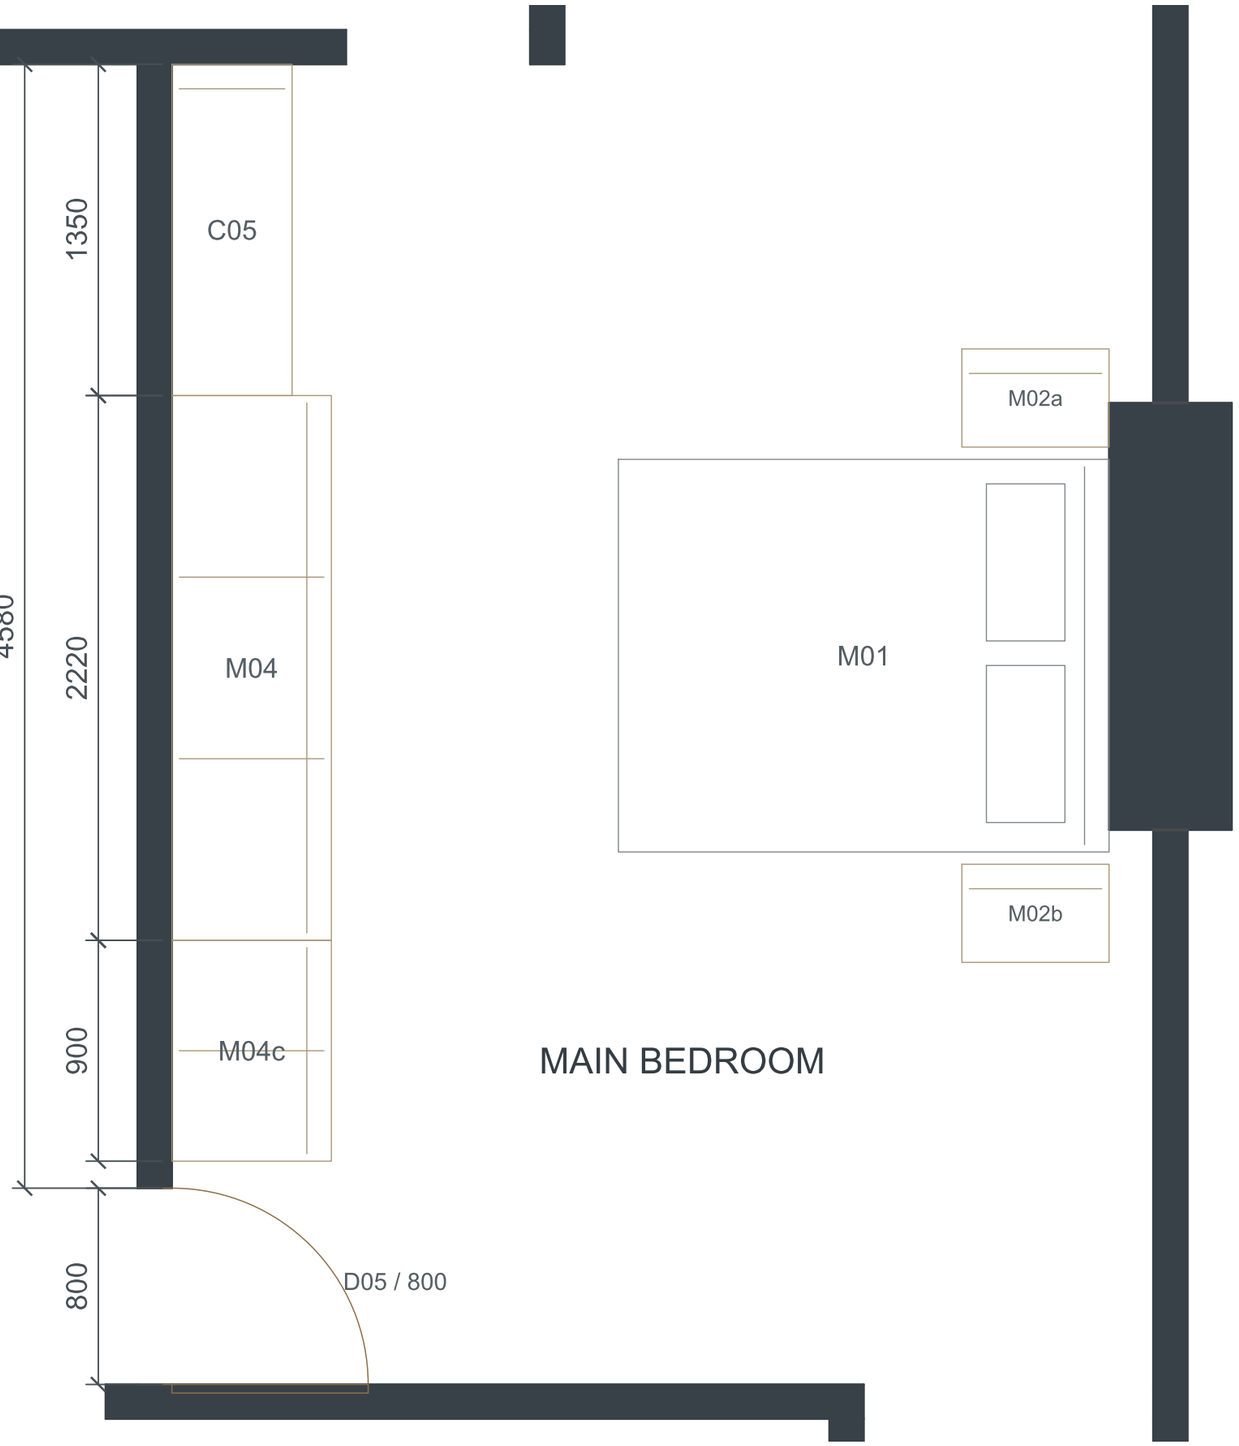

ONE MAIN WARDROBE / M04

2220 wide x 650 deep x 2150 high. This replaces the earlier interpretation of two 1075 mm bays. The complete unit has one continuous carcass in the website and one furniture block in CAD.

KHADIJA / M04c

900 wide x 650 deep x 2150 high. Its notebook dimensions remain intact.

WALL FIT

Internal wall before the doorway: 4580 mm. C05 dresser 1350 + M04 wardrobe 2220 + M04c wardrobe 900 = 4470 mm. Remaining allowance: 110 mm. The 800 mm door is additional to that wall length.

DRESSER AND BED

C05 stays 1350 x 490 mm. M01 stays 1600 x 2000; M02a / M02b each stay 600 x 400. Their positions and dimensions remain intact.

ENTRANCE / FLOOR

D05 returns to the west wall, at X=8720 and sheet Y=6270..7070. It opens inward through 90 degrees. The short return is removed; the doorway has one flush oak floor finish.


FIXED ARCHITECTURE

The bathroom/master wall stays straight at Y=1550..1690. All eight structural columns and the master balcony access remain unchanged.

Print A3 at 100%. Dimensions in millimetres.

Children bedroom / entrance and storage

Scale 1:25 at A3. One study desk retained on the right.

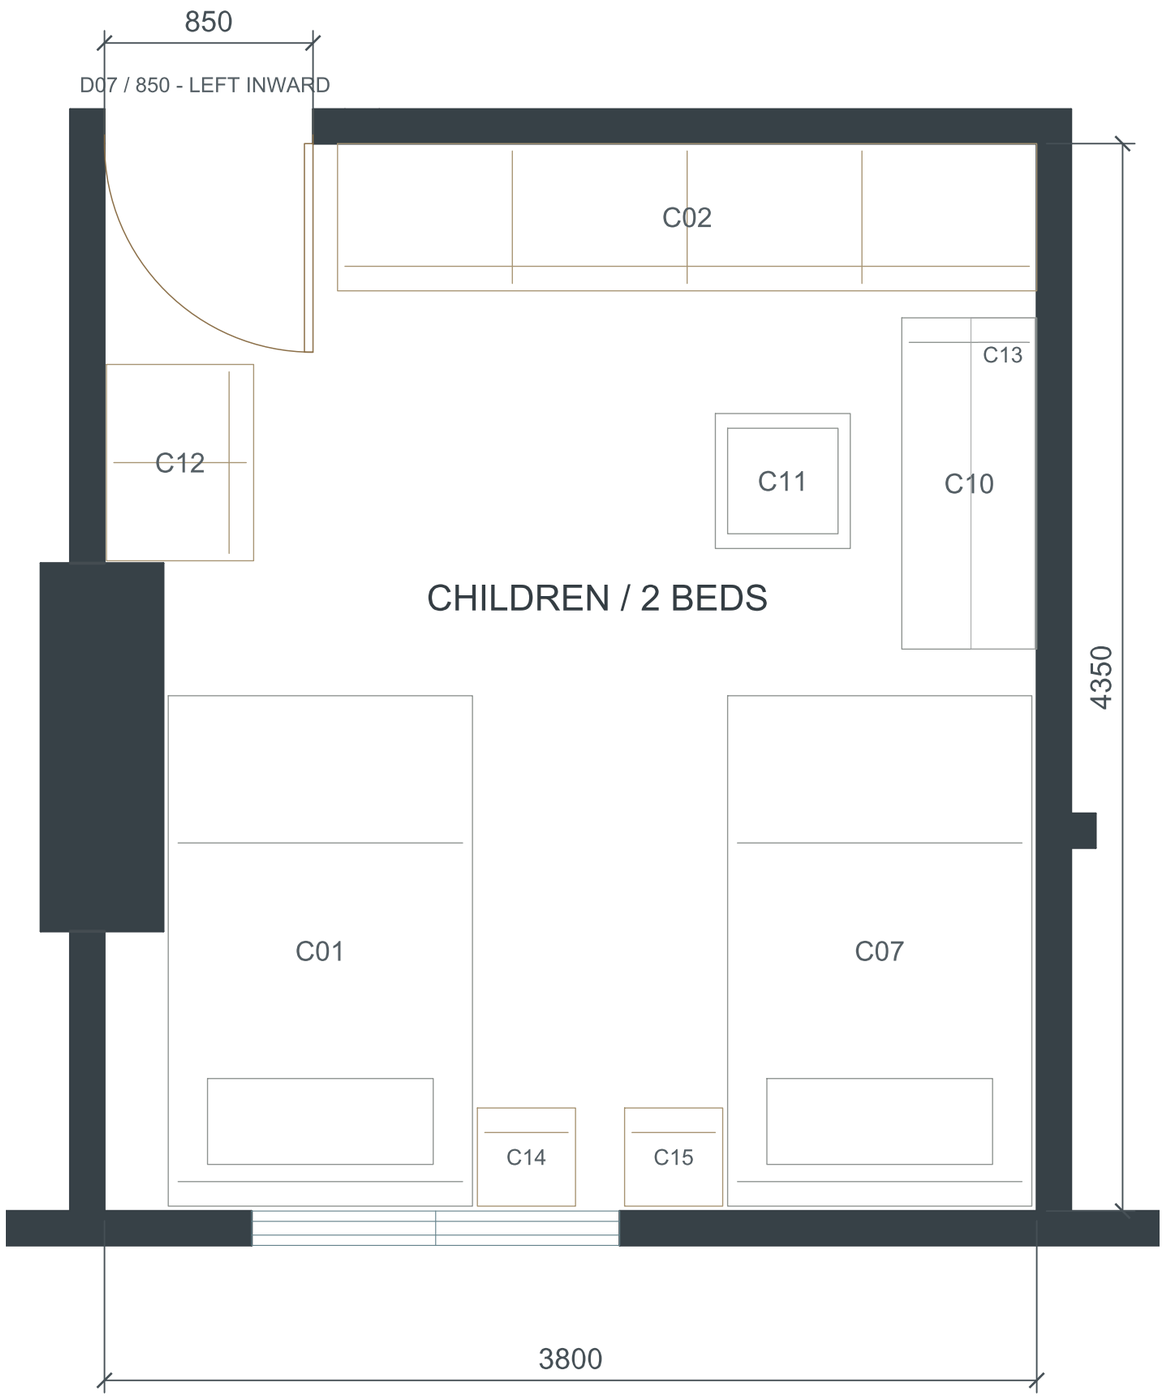

TWO BEDS

C01 / C07 use 1200 x 2000 mm mattresses in proposed 1240 x 2080 mm frames. Frame-to-frame aisle remains 1040 mm.

LEFT INWARD SWING

D07 hinges at the right jamb when viewed entering from the hall and swings toward the entrant left. Its leaf opens into the room, away from the storage fronts.

LEFT WARDROBE / C12

800 long x 600 deep x 2220 high, at sheet Y=8110..8910. It is shortened and set beyond the restored door swing, with 50 mm beyond the nominal leaf reach and 10 mm before the column.

ENTRANCE STORAGE / C02

C02 extends to 2850 x 600 mm, with a 100 mm reveal beside the restored door jamb. D07 returns to the opening at X=7600..8450, retaining its 850 mm width and left-inward swing.

STUDY

The right desk and chair remain. The short left hanging bookcase is removed; there is no left desk or chair.

DRAWING CHECK

CAD insert locations and door rotations are verified against the website data after native AutoCAD round-trip. Dimensions use millimetres throughout.

Print A3 at 100%. Dimensions in millimetres.