Furnished floor plan / R10

Scale 1:65 at A3. Shared layout for CAD and website.



ALL DIMENSIONS mm / WALLS >= 140 / STRUCTURAL COLUMNS RETAINED

140 mm WALLS

All wall and partition bands are at least 140 mm thick. The eight structural columns retain their original positions and sizes.

BEDROOMS MATCH

Main and children bedrooms are drawn from the same furniture records as the website, including both beds, wardrobe runs, dressing table and retained study desk.

CHILD DOOR

D07 retains its 850 mm nominal width. It now opens inward to the right of a person entering from the hall.

RESTORED ENTRANCES

The master and children openings return to their earlier wall positions. D05 stays 800 mm wide; the short master entry return is removed.

STORAGE

The short children wardrobe C12 directly ahead of the entrance is removed. Entrance-wall wardrobe C02 remains 2850 x 600 mm. The corrected master wardrobe remains one 2220 x 650 x 2150 high unit.


CHECKED

Native AutoCAD audit reports zero errors. Floor furniture and door swing sectors clear walls and columns. This is the R10 review set.

Print A3 at 100%. Dimensions in millimetres.

Main bedroom / corrected wardrobe and entrance

Scale 1:25 at A3. Owner-confirmed width and height.

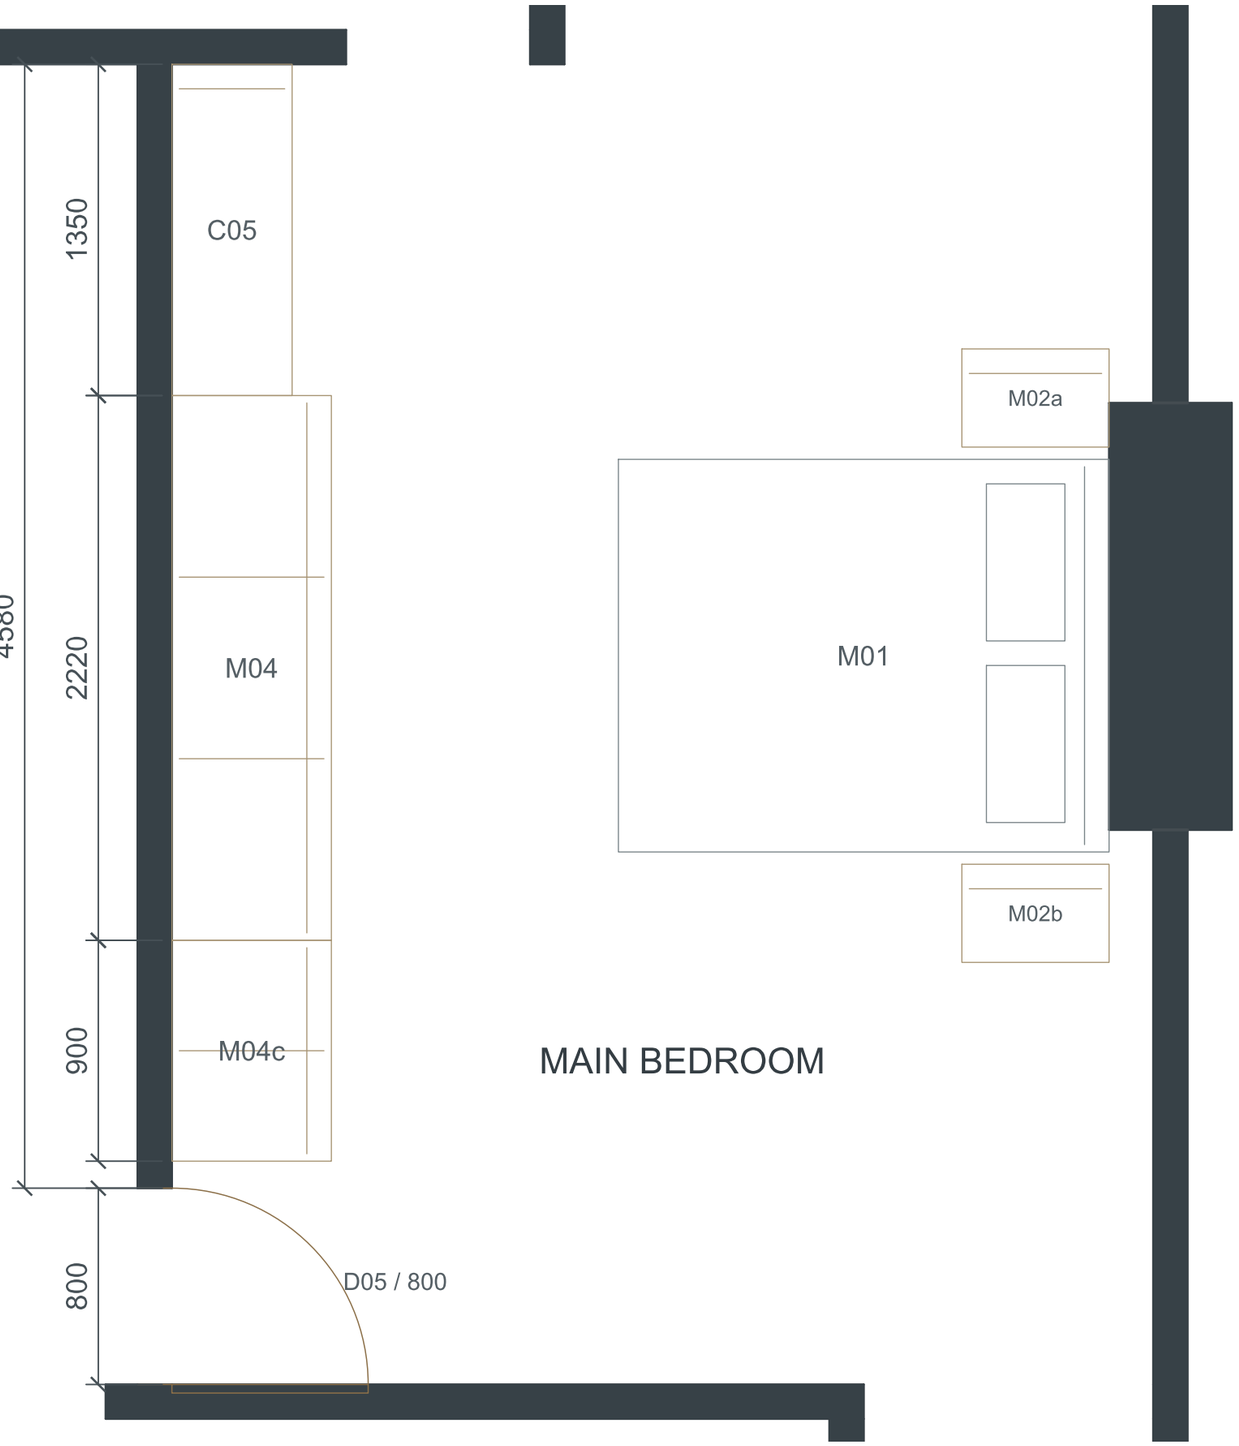

ONE MAIN WARDROBE / M04

2220 wide x 650 deep x 2150 high. This replaces the earlier interpretation of two 1075 mm bays. The complete unit has one continuous carcass in the website and one furniture block in CAD.

KHADIJA / M04c

900 wide x 650 deep x 2150 high. Its notebook dimensions remain intact.

WALL FIT

Internal wall before the doorway: 4580 mm. C05 dresser 1350 + M04 wardrobe 2220 + M04c wardrobe 900 = 4470 mm. Remaining allowance: 110 mm. The 800 mm door is additional to that wall length.

DRESSER AND BED

C05 stays 1350 x 490 mm. M01 stays 1600 x 2000; M02a / M02b each stay 600 x 400. Their positions and dimensions remain intact.

ENTRANCE / FLOOR

D05 returns to the west wall, at X=8720 and sheet Y=6270..7070. It opens inward through 90 degrees. The short return is removed; the doorway has one flush oak floor finish.


FIXED ARCHITECTURE

The bathroom/master wall stays straight at Y=1550..1690. All eight structural columns and the master balcony access remain unchanged.

Print A3 at 100%. Dimensions in millimetres.

Children bedroom / entrance and storage

Scale 1:25 at A3. One study desk retained on the right.

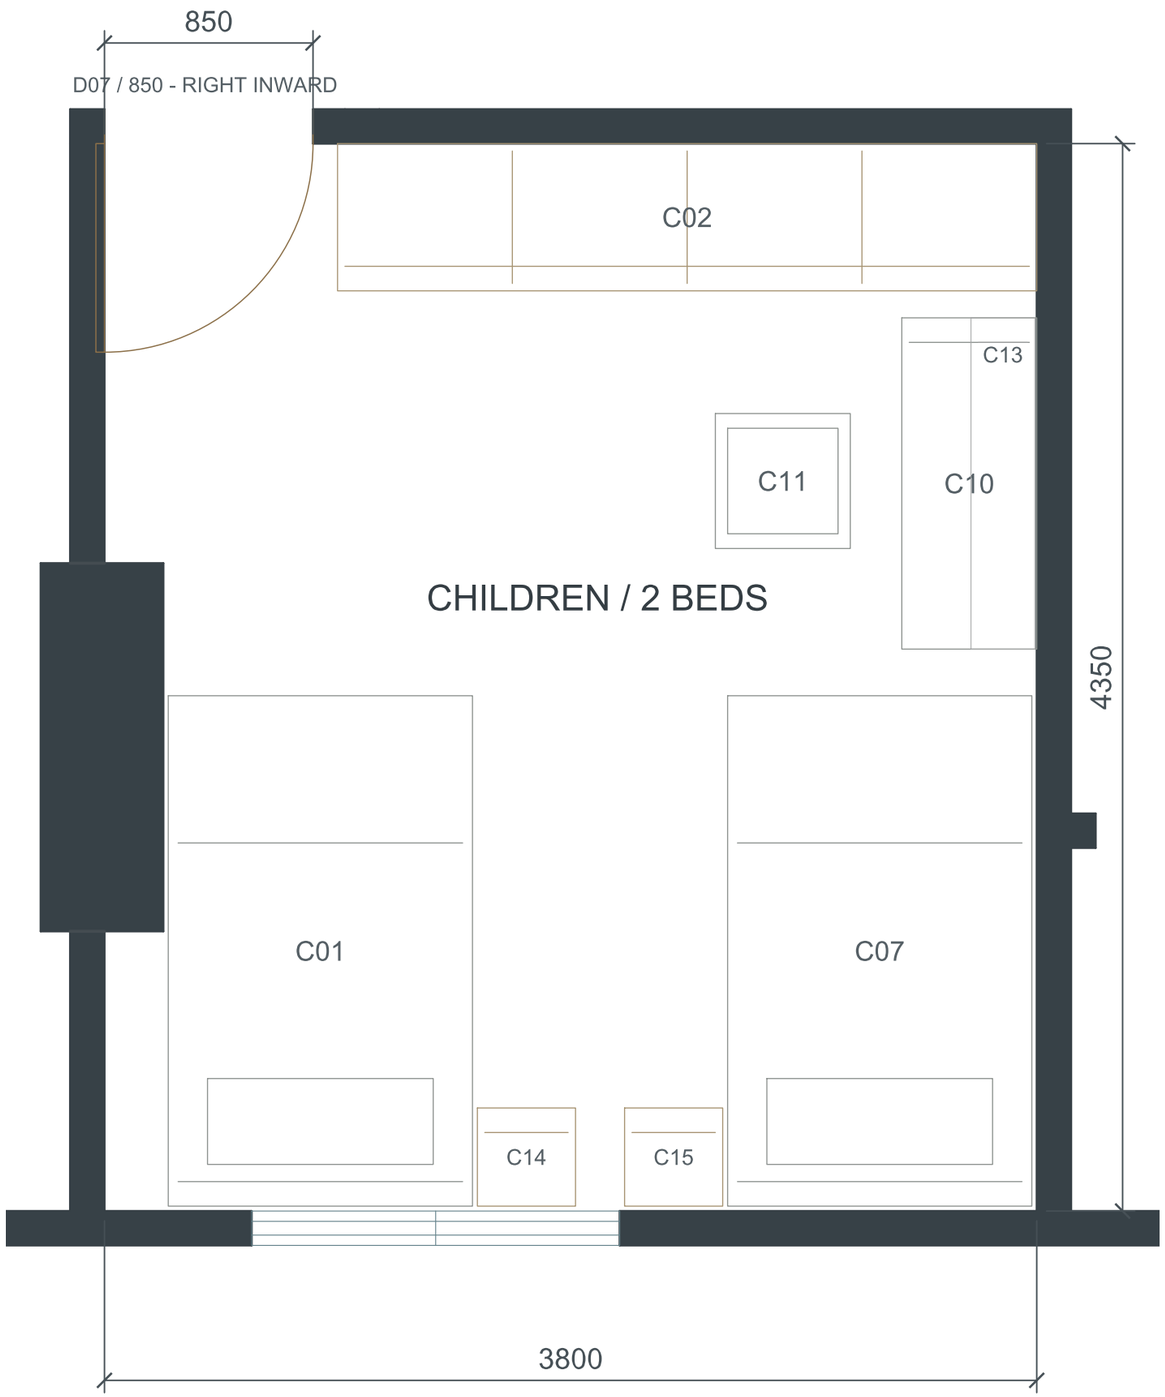

TWO BEDS

C01 / C07 use 1200 x 2000 mm mattresses in proposed 1240 x 2080 mm frames. Frame-to-frame aisle remains 1040 mm.

RIGHT INWARD SWING

D07 hinges at the west jamb (right-hand side when entering from the hall) and opens inward toward the entrant right. The 850 mm doorway position and width are retained.

ENTRY CLEARED / C12 REMOVED

The short left-wall wardrobe directly ahead of the doorway is removed from both CAD and the website. Its former footprint at sheet X=7608..8208, Y=8110..8910 is clear floor again.

ENTRANCE STORAGE / C02

C02 is 2850 x 600 mm, with a 100 mm reveal beside the door jamb. D07 remains at X=7600..8450, retaining its 850 mm width with the new right-inward swing.

STUDY

The right desk and chair remain. The short left hanging bookcase is removed; there is no left desk or chair.

DRAWING CHECK

CAD insert locations and door rotations are verified against the website data after native AutoCAD round-trip. Dimensions use millimetres throughout.

Print A3 at 100%. Dimensions in millimetres.