Furnished floor plan / R07

Scale 1:65 at A3. Shared layout for CAD and website.



ALL DIMENSIONS mm / WALLS >= 140 / STRUCTURAL COLUMNS RETAINED

140 mm WALLS

All wall and partition bands are at least 140 mm thick. The eight structural columns retain their original positions and sizes.

BEDROOMS MATCH

Main and children bedrooms are drawn from the same furniture records as the website, including both beds, wardrobe runs, dressing table and retained study desk.

CHILD DOOR

D07 retains its 850 mm nominal width. It opens inward to the left of a person entering from the hall.

SHELF REPLACEMENT

C12 replaces the short left-wall hanging shelf beside the entrance with an 800 wide x 600 deep x 2220 high wardrobe in the matching finish.

MASTER FIT

The bathroom/master partition shifts 60 mm north. This keeps the recorded 4400 mm dresser/wardrobe run, the new 140 mm return and the 900 mm entrance.


CHECKED

Native AutoCAD audit reports zero errors. Floor furniture and door swing sectors clear walls and columns. This is the R07 review set.

Print A3 at 100%. Dimensions in millimetres.

Main bedroom / furniture and wall detail

Scale 1:25 at A3. Recorded furniture envelopes retained.

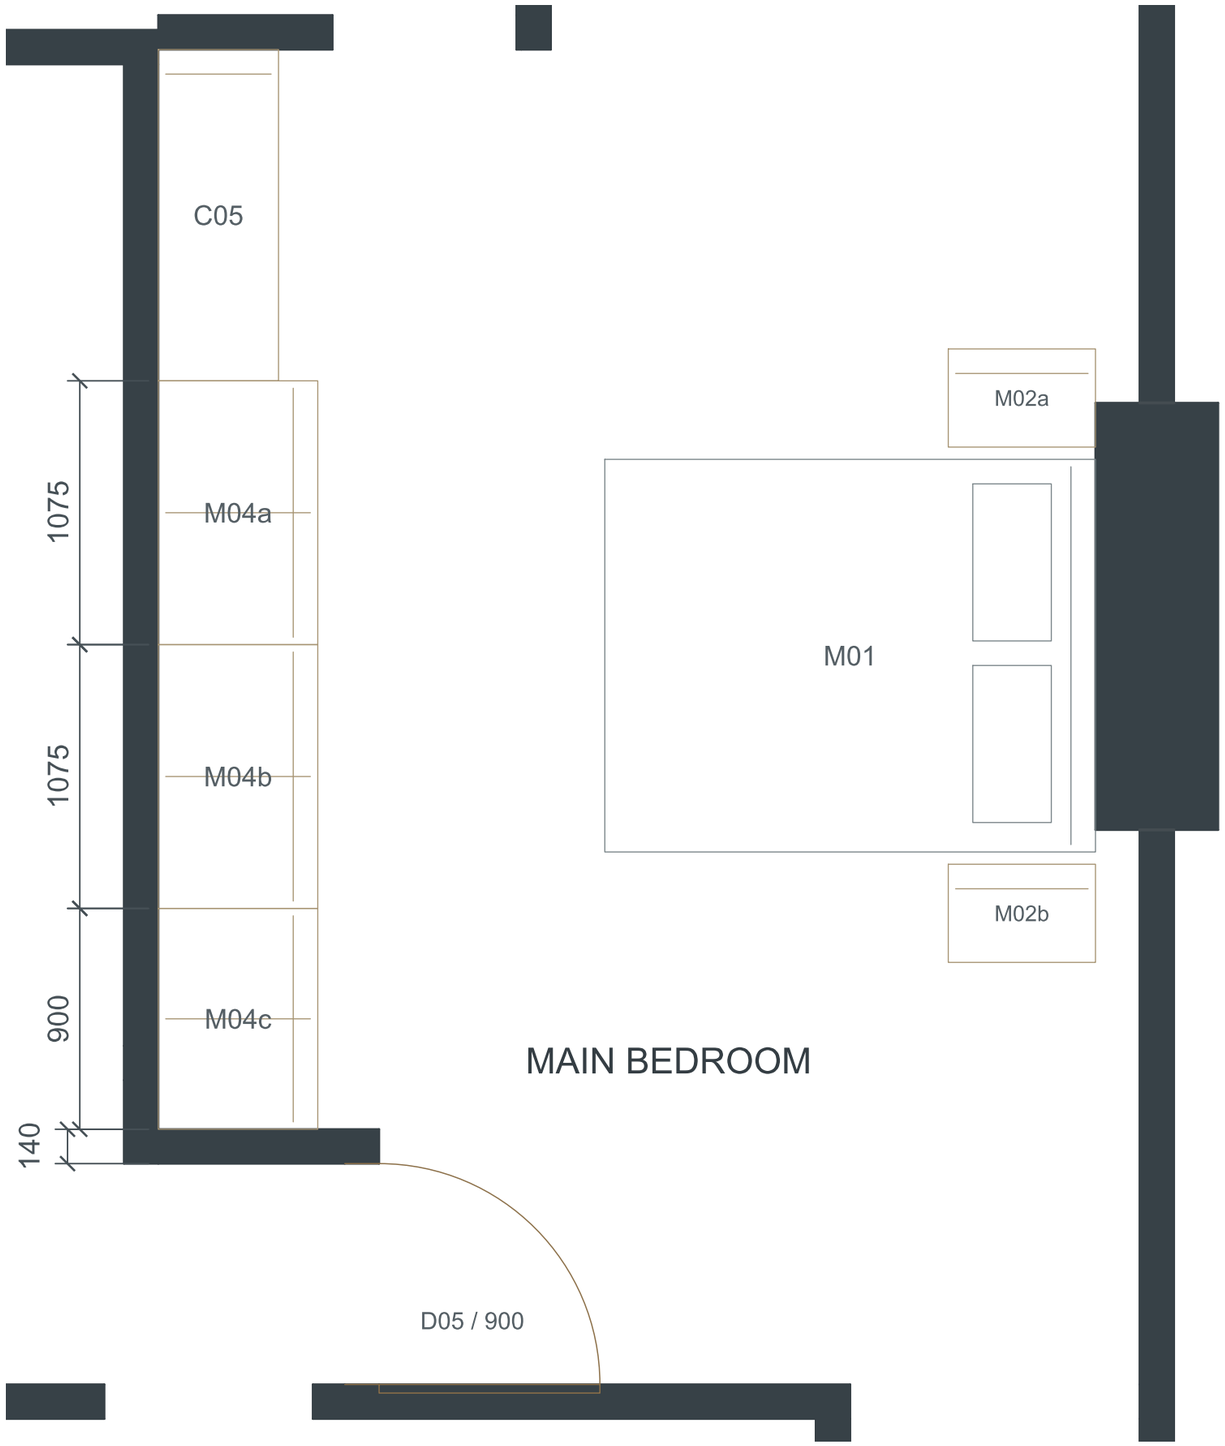

RECORDED WARDROBES

M04a and M04b remain 1075 wide x 650 deep x 2220 high each. Together they represent the recorded 2150 mm main wardrobe.

KHADIJA / M04c

900 wide x 650 deep x 2150 high. Its notebook dimensions remain intact.

DRESSING TABLE

C05 remains 1350 wide x 490 deep. It starts at sheet Y=1630, followed continuously by the three wardrobe bays. Total run: 4400 mm.

BED AND TABLES

M01 remains 1600 x 2000 mm. M02a / M02b each remain 600 x 400 mm. Bed faces from the right; wardrobe and dresser face from the left.

ENTRANCE

D05 is 900 mm wide at X=9620, sheet Y=7070. The 140 mm return occupies sheet Y=6030 to 6170. The old west opening remains an open link from the hall.


BALCONY ROUTE

An open passage leads into the recess. The glazed entrance stays at the former divider farther inside the balcony. Access remains from the master bedroom.

Print A3 at 100%. Dimensions in millimetres.

Children bedroom / entrance and storage

Scale 1:25 at A3. One study desk retained on the right.

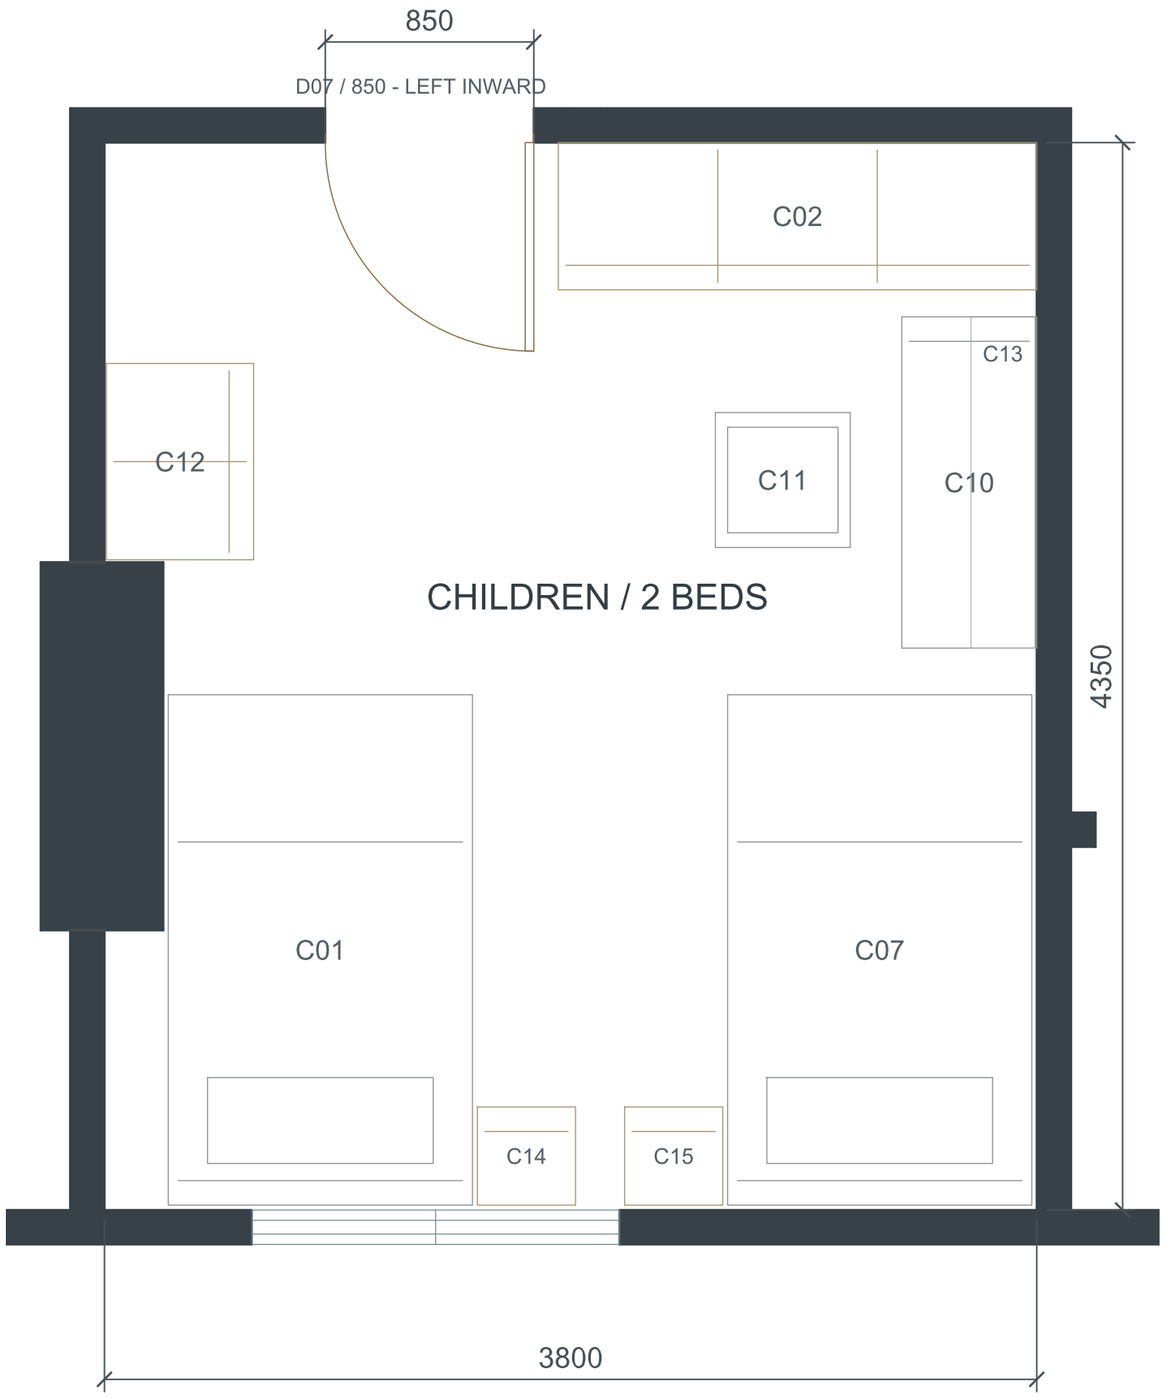

TWO BEDS

C01 / C07 use 1200 x 2000 mm mattresses in proposed 1240 x 2080 mm frames. Frame-to-frame aisle remains 1040 mm.

LEFT INWARD SWING

D07 hinges at the right jamb when viewed entering from the hall and swings toward the entrant left. Its leaf opens into the room, away from the storage fronts.

NEW C12 WARDROBE

800 wide x 600 deep x 2220 high, on the left wall beside the entrance. Two sliding fronts match the warm-white wardrobe finish.

ENTRANCE STORAGE

C02 remains 1950 x 600 mm with the approved shortening. It leaves a 100 mm reveal beside the door jamb.

STUDY

The right desk and chair remain. The short left hanging bookcase is removed; there is no left desk or chair.

DRAWING CHECK

CAD insert locations and door rotations are verified against the website data after native AutoCAD round-trip. Dimensions use millimetres throughout.

Print A3 at 100%. Dimensions in millimetres.